
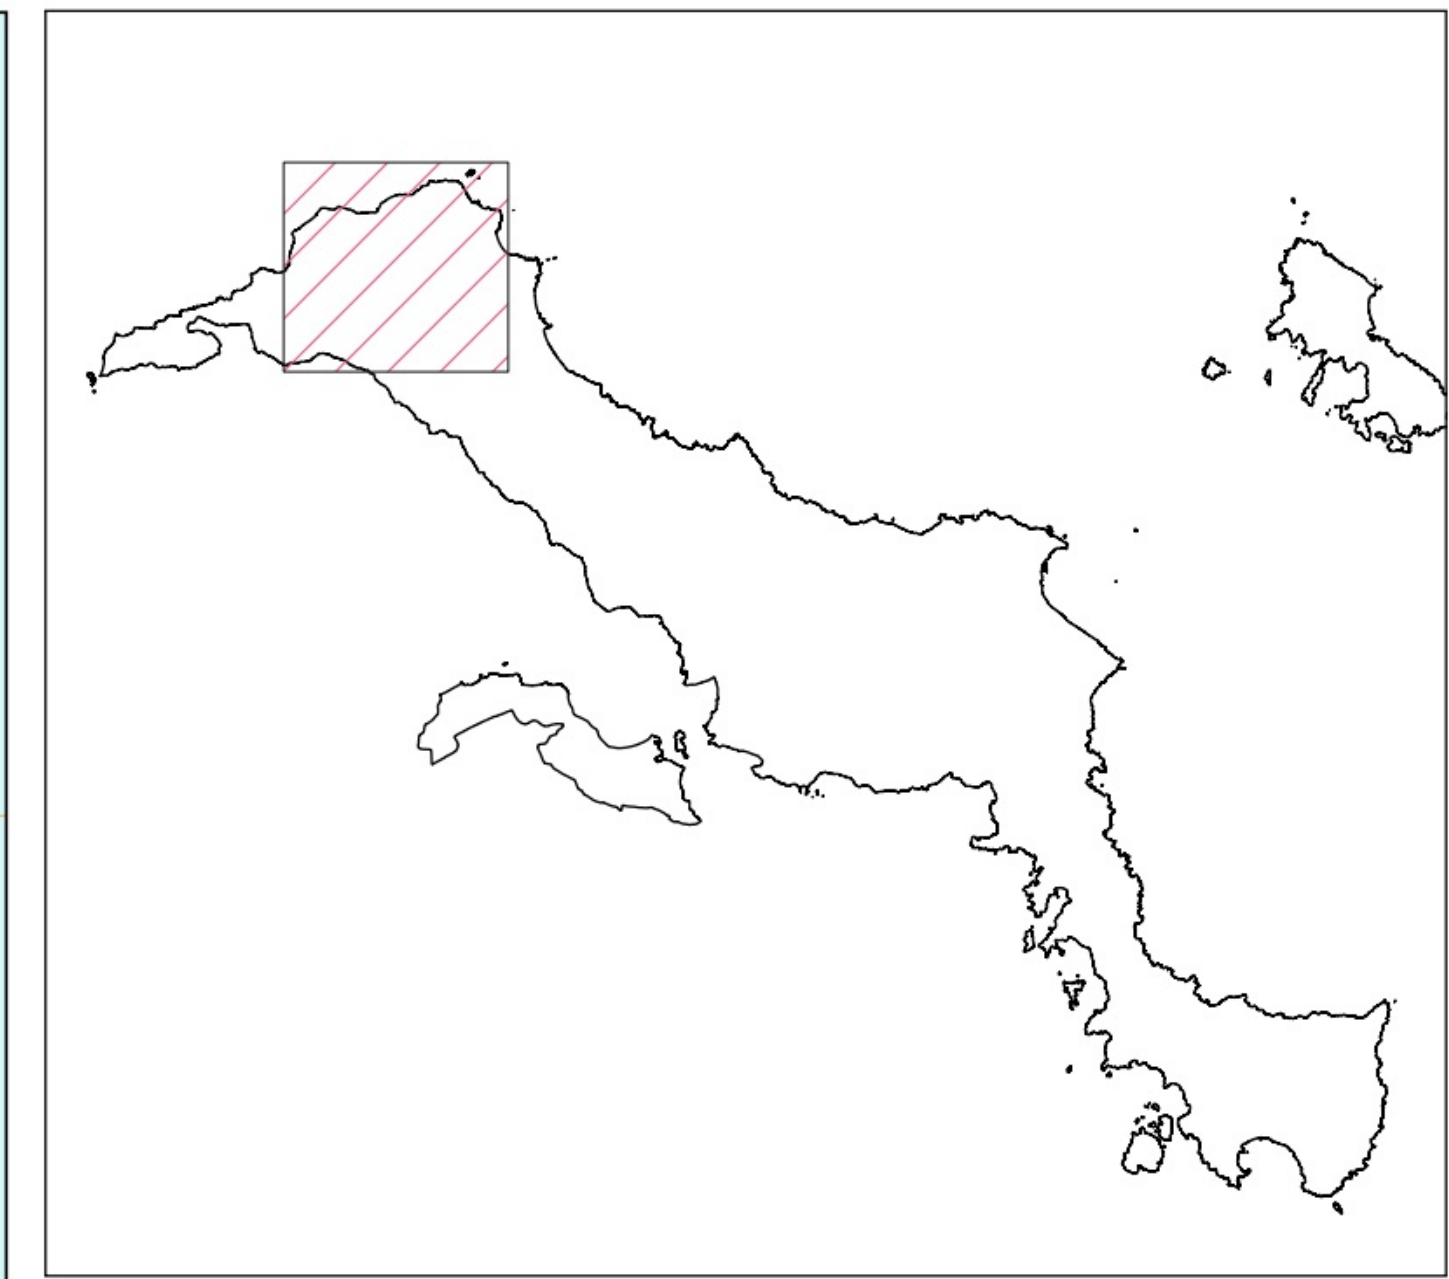


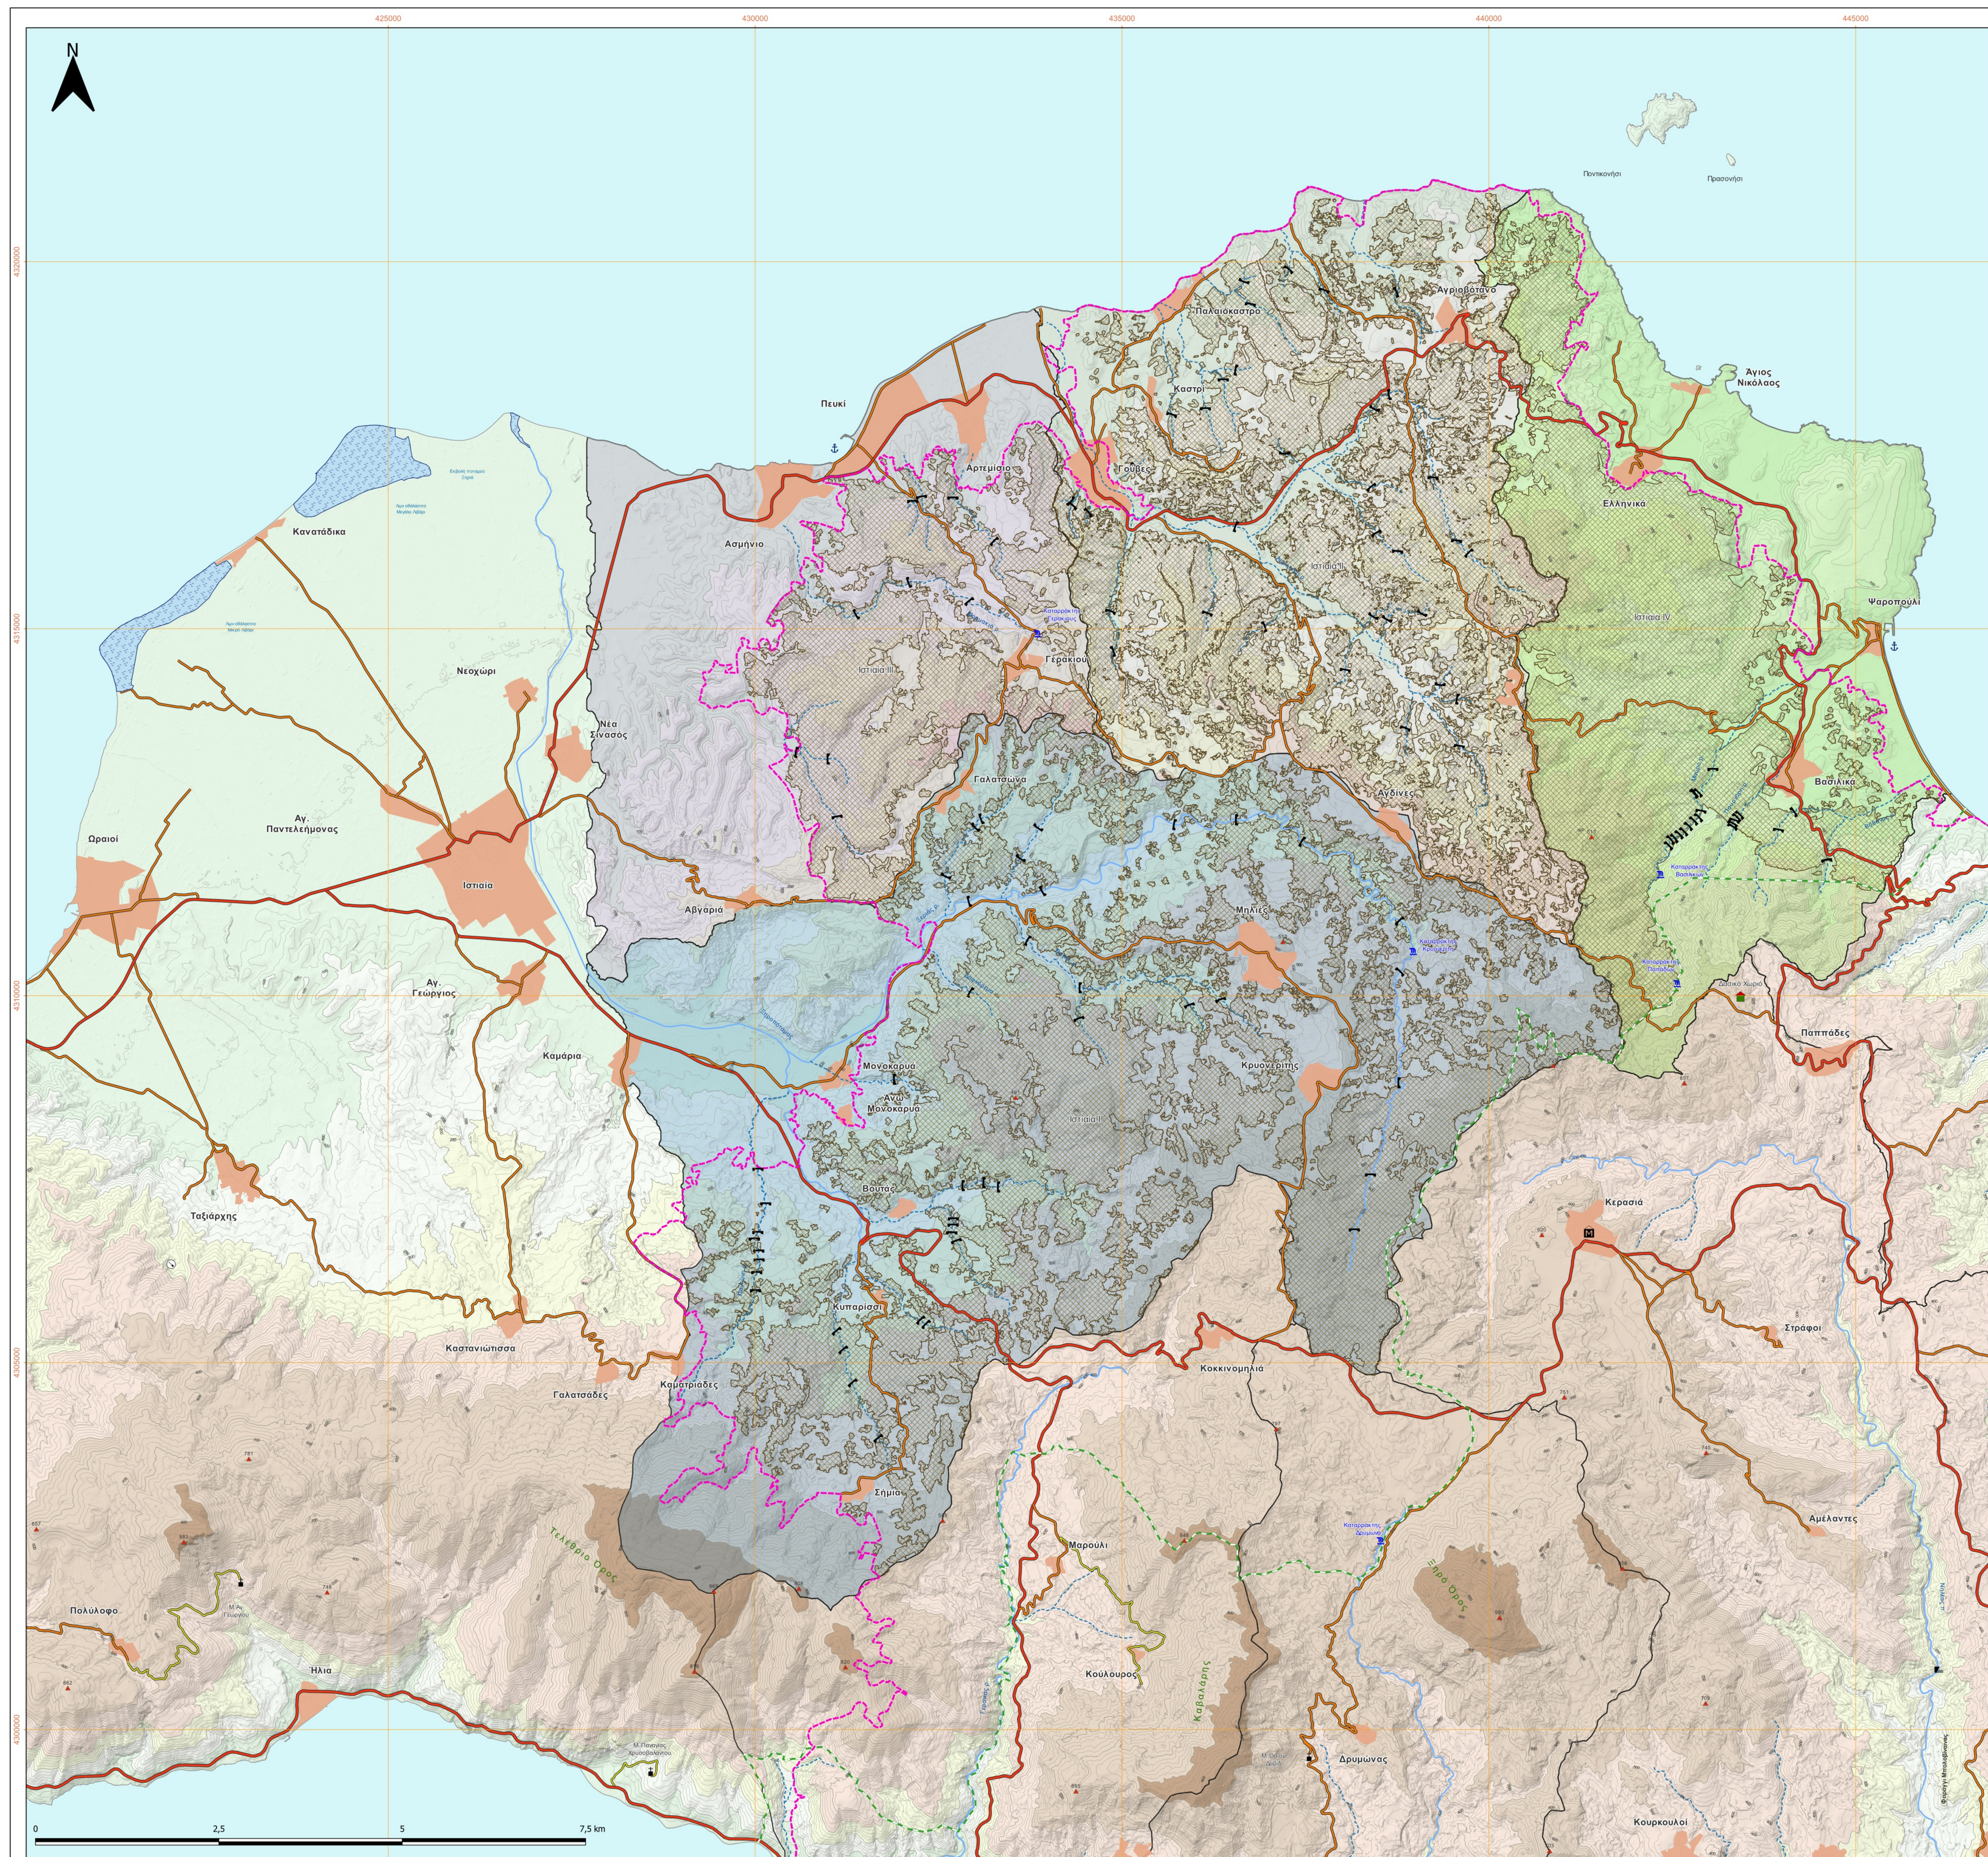

ΥΠΟΜΗΝΗΜΑ

Όριο πυρκαγιάς Αυγούστου 2021

Όριο Δασοαρχείου Άλμης - Ιστιαίας

Οικισμός

Υγρότοπος

Λίμνη

Ποτάμιο - ρέματα μόνιμης ροής

Ρέματα περιοδικής ροής

Λεκάνες απορροής Ιστιαίας

Ιστιαία I

Ιστιαία II

Ιστιαία III

Ιστιαία IV

Φράγμα βάρους

Περιοχή κορυμμοειδών Δασοαρχείου Ιστιαίας

Φαράγγι

Καταράκτης

Μοναστήρι

Δασικό χωριό

Μουσείο Απολιθωμένων Θηλαστικών

Κορυφή

Λίμνη

Λίμνη μικρών σκαφών

Κύριος δρόμος

Ασφαλτοστρωμένος δρόμος

Χωματόδρομος

Ισομείς καμπύλες, Ισοδιάσταση 100 μ.

Ισομείς καμπύλες, Ισοδιάσταση 20 μ.

Λεκάνη απορροής	Περιγραφή	Εκταση (στρ)
Ιστιαία I	Υδρολογική Λεκάνη 23.27.01 "Χαλμαρός Σπράς Ιστιαίας" (Ιστιαία I)	91.751,45
Ιστιαία II	Υδρολογική Λεκάνη 23.27.02 "Χαλμαρότα Χαλμαρών Ασημένιου-Βασιλικών" (Ιστιαία II)	48.518,87
Ιστιαία III	Υδρολογική Λεκάνη 23.27.01 "Χαλμαρός Σπράς Ιστιαίας" (Ιστιαία III)	40.046,65
Ιστιαία IV	Υδρολογική Λεκάνη 23.27.02 "Χαλμαρότα Χαλμαρών Ασημένιου-Βασιλικών" (Ιστιαία IV)	43.942,68



ΠΡΟΓΡΑΜΜΑ ΑΝΑΣΥΓΚΡΟΤΗΣΗΣ
ΒΟΡΕΙΑΣ ΕΥΒΟΙΑΣ

MASTER PLAN ΓΙΑ ΤΟ ΝΕΟ ΔΑΣΟΣ

ΤΙΤΛΟΣ ΣΧΕΔΙΟΥ:
**ΧΑΡΤΗΣ ΑΝΤΙΠΛΗΜΜΥΡΙΚΩΝ ΕΡΓΩΝ
ΔΑΣΑΡΧΕΙΟΥ ΙΣΤΙΑΙΑΣ**

ΑΡΙΘΜΟΣ ΣΧΕΔΙΟΥ:
4.2

ΚΛΙΜΑΚΑ:
1:30.000

ΗΜΕΡΟΜΗΝΙΑ ΣΥΝΤΑΞΗΣ:
ΝΟΕΜΒΡΙΟΣ 2021

ΜΕΛΕΤΗΤΗΣ:


Μεσοποταμίας 9, Τ.Κ. 10482, Άθινα
Τηλ: 210 3213605 • Τεlex: 210 3216904
info@forest.gr • www.forest.gr

ΓΙΑ ΤΟΝ ΜΕΛΕΤΗΤΗ:

ΑΠΟΣΤΟΛΗΣ ΗΛΙΑΣ
ΝΟΜΙΜΟΣ ΕΚΠΡΟΣΩΠΟΣ

ΕΛΕΓΧΘΗΚΕ

ΥΠΕΥΘΥΝΟΣ ΤΟΜΕΑ ΜΕΛΕΤΩΝ

ΕΓΚΡΙΣΗ

ΥΠΕΥΘΥΝΟΣ ΤΜΗΜΑΤΟΣ ΧΑΡΤΟΓΡΑΦΗΣΗΣ & GIS

Αναθεώρηση

Περιγραφή

Ημερομηνία

1

2