
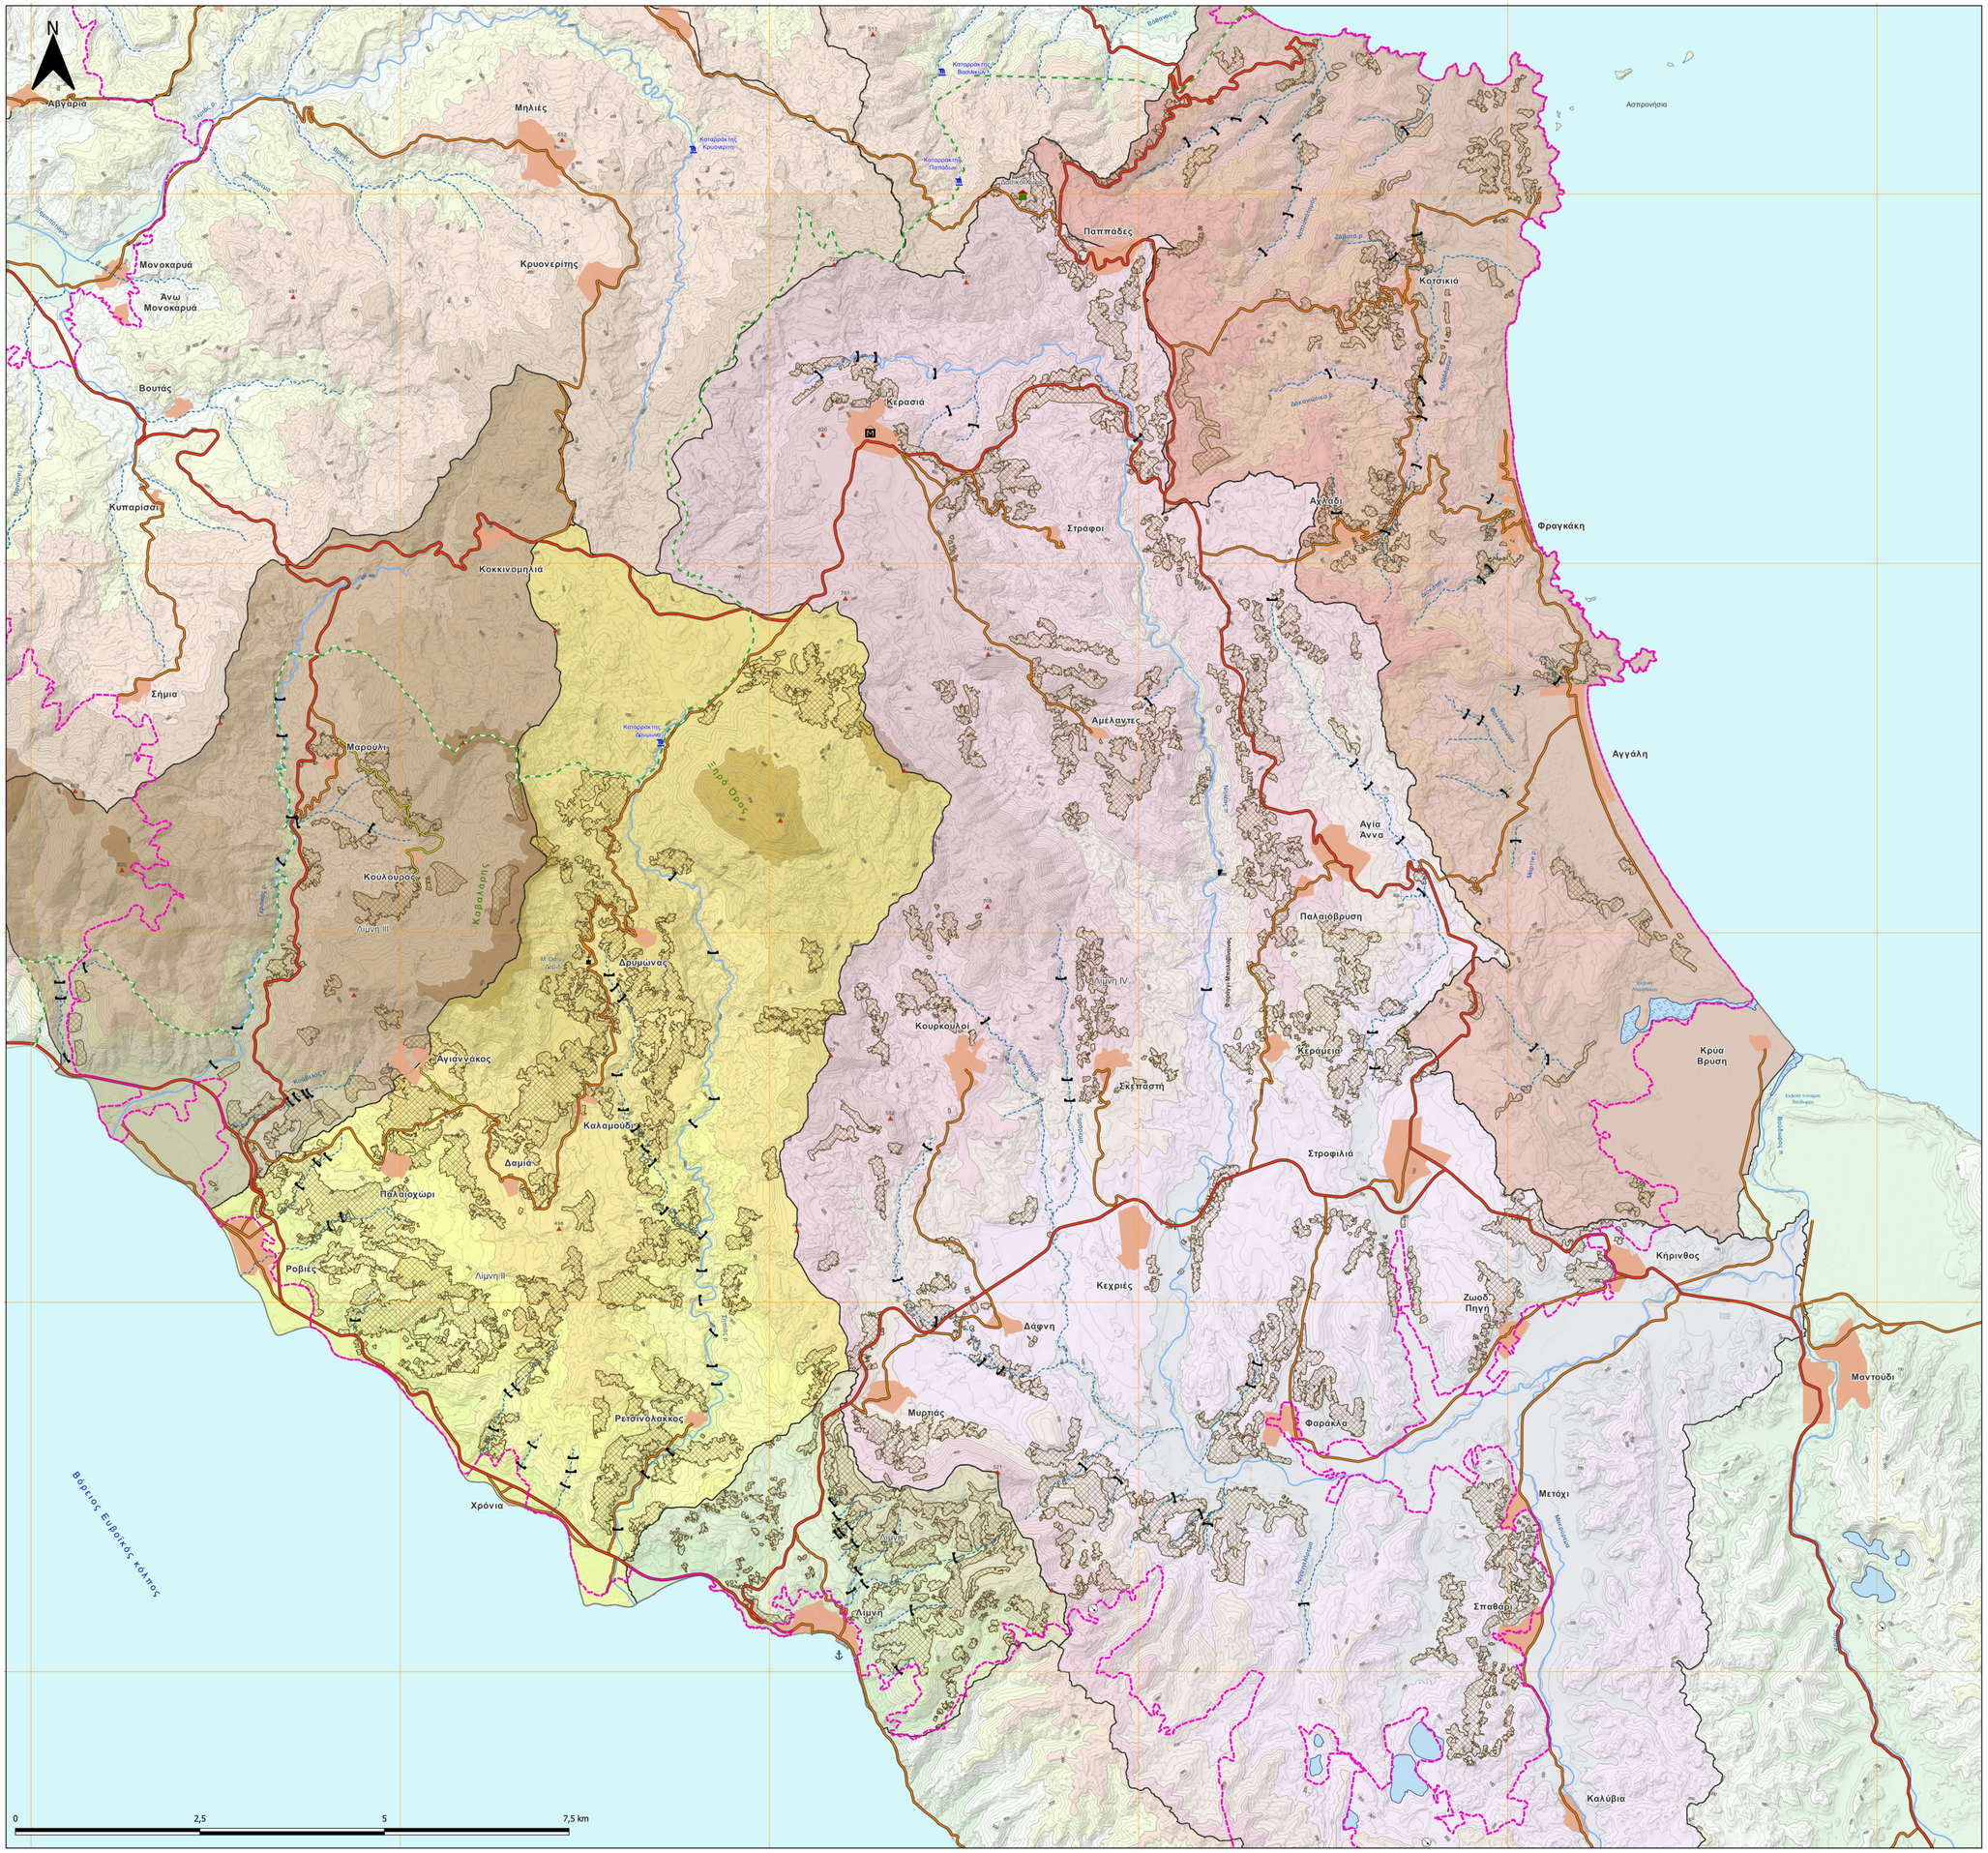


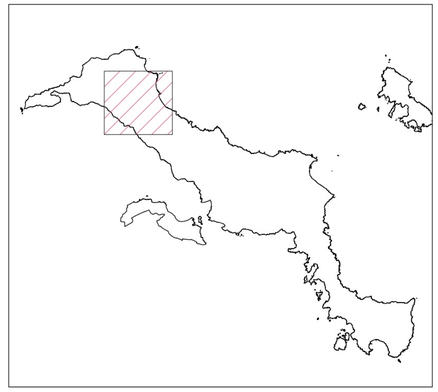

ΥΠΟΜΝΗΜΑ

- Όριο πυρκαγιάς Αυγούστου 2021
- Όριο Δασαρχείων Λίμνης - Ιστιαίας
- Οικισμός
- Υγρότοπος
- Λίμνη
- Ποτάμια - ρέματα μόνιμης ροής
- Ρέματα περιοδικής ροής

Λεκάνες απορροής Λίμνης

- Λίμνη Ι
- Λίμνη ΙΙ
- Λίμνη ΙΙΙ
- Λίμνη IV
- Λίμνη V
- Φράγμα βάρους
- Περιοχή κορμοδεμάτων Δασαρχείου Λίμνης
- Φαράγγι
- Καταρράκτης
- Μοναστήρι
- Δασικό χωριό
- Μουσείο Απολιθωμένων Θηλαστικών
- Κορυφή
- Λιμάνι
- Λιμάνι μικρών σκαφών
- Κύριος δρόμος
- Ασφαλτοστρωμένος δρόμος
- Χωματόδρομος
- Ισοϋψείς καμπύλες, Ισοδιάσταση 100 μ.
- Ισοϋψείς καμπύλες, Ισοδιάσταση 20 μ.

Λεκάνη απορροής	Περιγραφή	Έκταση (στρ)
Λίμνη Ι	Υδρολογική Λεκάνη 23.27.08 "Συγκρότημα Υπολεκανών Νδ κλιτών Κανδυλίου Όρους" (Λίμνη Ι)	13.403,45
Λίμνη ΙΙ	Υδρολογική Λεκάνη 23.27.06 "Χείμαρρος Σημάδος" (Λίμνη ΙΙ)	70.535,01
Λίμνη ΙΙΙ	Υδρολογική Λεκάνη 23.27.05 "Χείμαρρος Γερόνα" (Λίμνη ΙΙΙ)	47.037,26
Λίμνη IV	Υδρολογική Λεκάνη 23.27.07.01 "Χείμαρρος Βοσδουρου - Νηλιώς" (Λίμνη IV)	20.6827,401
Λίμνη V	Υδρολογική Λεκάνη 23.27.02 "Συγκρότημα Χειμάρρων Ασημένου-Βασιλικών" (Λίμνη V)	65.103,241

ΠΡΟΓΡΑΜΜΑ ΑΝΑΣΥΓΚΡΟΤΗΣΗΣ ΒΟΡΕΙΑΣ ΕΥΒΟΙΑΣ

MASTER PLAN ΓΙΑ ΤΟ ΝΕΟ ΔΑΣΟΣ

ΤΙΤΛΟΣ ΣΧΕΔΙΟΥ:
ΧΑΡΤΗΣ ΑΝΤΙΠΛΗΜΜΥΡΙΚΩΝ ΕΡΓΩΝ ΔΑΣΑΡΧΕΙΟΥ ΛΙΜΝΗΣ

ΑΡΙΘΜΟΣ ΣΧΕΔΙΟΥ: **4.1**

ΚΛΙΜΑΚΑ: 1:30.000

ΗΜΕΡΟΜΗΝΙΑ ΣΥΝΤΑΞΗΣ: ΝΟΕΜΒΡΙΟΣ 2021

ΜΕΛΕΤΗΤΗΣ:
ΔΙΑΧΕΙΡΙΣΗ ΚΑΙ ΠΡΟΣΤΑΣΙΑ ΠΕΡΙΒΑΛΛΟΝΤΟΣ
Μαυρομιχάλη 9, Τ.Κ. 10682 Αθήνα
Τηλ: 2102213093 • Fax: 2102216704
info@forest.gr • www.forest.gr

ΓΙΑ ΤΟΝ ΜΕΛΕΤΗΤΗ:
ΑΠΟΣΤΟΛΙΔΗΣ ΗΛΙΑΣ
ΝΟΜΙΜΟΣ ΕΚΠΡΟΣΩΠΟΣ

ΕΛΕΓΧΘΗΚΕ	ΥΠΕΥΘΥΝΟΣ ΤΟΜΕΑ ΜΕΛΕΤΩΝ
	ΥΠΕΥΘΥΝΟΣ ΤΜΗΜΑΤΟΣ ΧΑΡΤΟΓΡΑΦΗΣΗΣ & GIS
ΕΓΚΡΙΣΗ	

Αναθεώρηση	Περιγραφή	Ημερομηνία
1		
2		